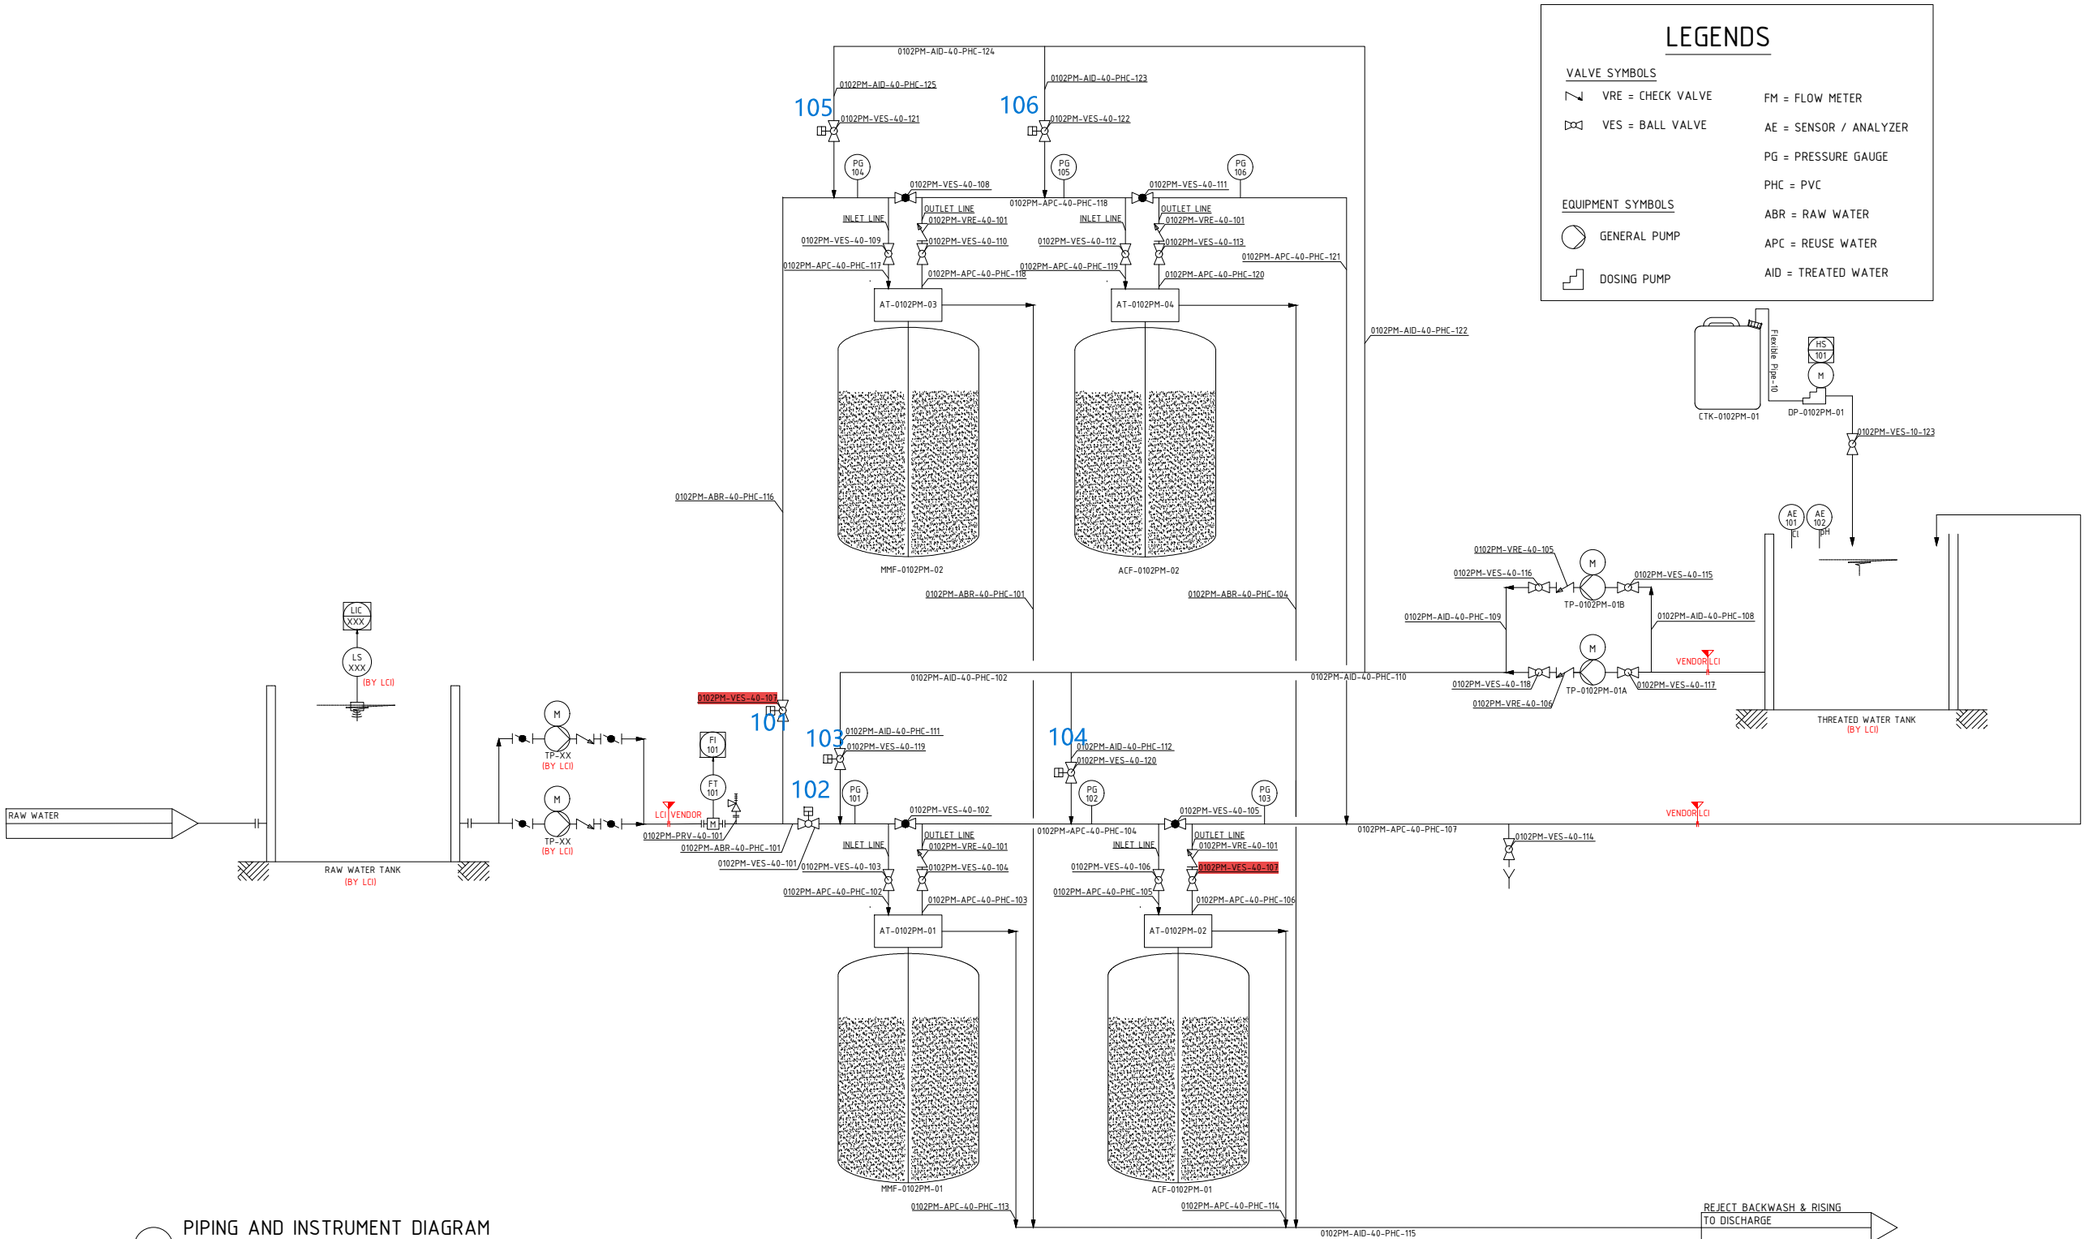


PIPING AND INSTRUMENT DIAGRAM

TAG.NO	TP-0102PM-01A/B
EQUIPMENT	FILTER BACKWASH PUMP
TYPE.	VERTICAL MULTISTAGE PUMP
CAPACITY	21.27 CMH HEAD 2 BAR
POWER	2.2 kW
QTY.	2 UNIT

TAG.NO	MMF-0102PM-01/02
EQUIPMENT	MULTI MEDIA FILTER
VOLUME	D = 36 inch, H = 72 inch
MATERIAL	FRP
QTY.	2 UNIT

TAG.NO	ACF-0102PM-01/02
EQUIPMENT	ACTIVATED CARBON FILTER
VOLUME	D = 36 inch, H = 72 inch
MATERIAL	FRP
QTY.	2 UNIT

TAG.NO	CTK-0102PM-01
EQUIPMENT	CHLORINATION CHEMICAL TANK
VOLUME	25 L
MATERIAL	PE
QTY.	1 UNIT

TAG.NO	DP-0102PM-01
EQUIPMENT	CHLORINATION DOSING PUMP
CAPACITY	0.4 LPH
POWER	0.013 kW
QTY.	1 UNIT

TAG.NO	AT-0102PM-01/02/03/04
EQUIPMENT	AUTOTROL

NOTES

REFERENCE DOCUMENTS

REV.	I.T.	DESCRIPTION	BY	DWG.	CKD.	APPR.	AUTH.	DATE
B	A	ISSUED FOR INTERNAL REVIEW	TA	TA	AT	DW	OR	26/12/2025
A	A	ISSUED FOR INTERNAL REVIEW	TA	TA	AT	DW	OR	25/06/2025

REVISIONS

I.T. ISSUE TYPE: (A) PRELIMINARY (B) FOR APPROVAL (C) FOR INFORMATION (D) FOR QUOTATION (E) FOR CONSTRUCTION (F) AS PURCHASED (G) AS BUILT (H) CANCELLED

VALE | LEIGHTON

CLASSIFICATION: CONFIDENTIAL

PROJECT: IGP – INTEGRATED MINES POMALAA (IMP)

PROJECT No. OR SE:

DETAILED DESIGN PROJECT

CONTRACT No.: –

OPERATION CAMP AREA

WATER TREATMENT PLANT

PIPING & INSTRUMENTATION DIAGRAM

SCALE	CONTRACTOR'S No.	VALE No.	REVISION
–	–	DF-FG-0102PM-P-94209-24	B